
C1_A - Basement Wall

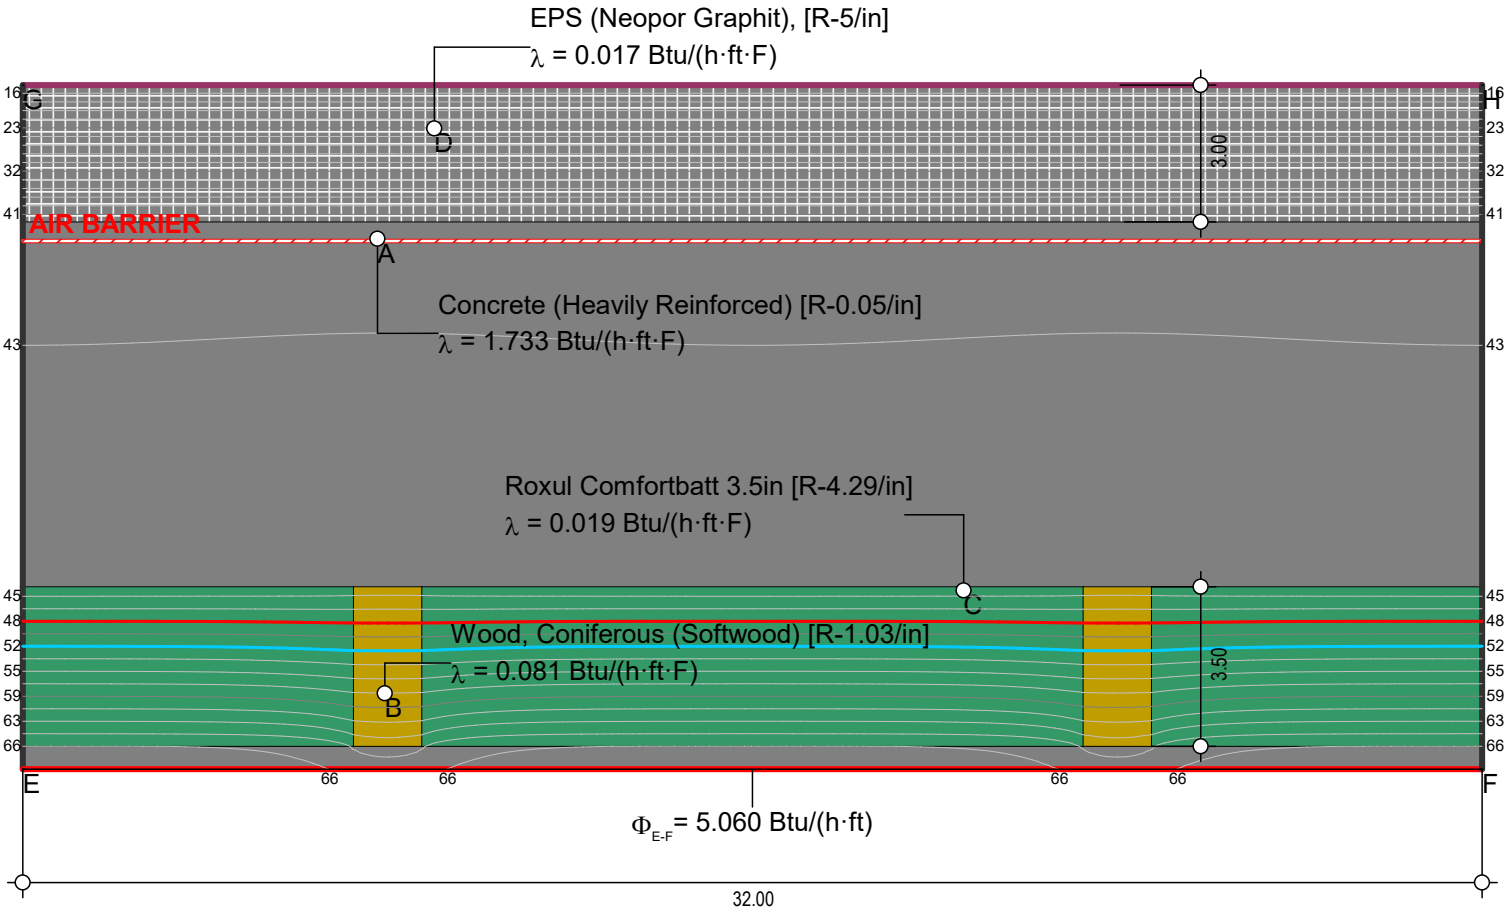

$$R_{eq\ E\text{-}F} = \frac{54.0 \cdot 2.667}{5.06} = 28.5\ F \cdot ft^2 \cdot h/Btu$$

Boundary Condition	q[Btu/(h·ft²)]	θ[°F]	h[Btu/(h·ft²·F
Ext. No Rse		14.000	17.6
Interior, normal, horizontal		68.000	1.3
Symmetry/Model section	0.000		

Material	λ[Btu/(h·ft·F)]	ε
Concrete (Heavily Reinforced) [R-0.05/in]	1.733	0.900
EPS (Neopor Graphit), [R-5/in]	0.017	0.900
GWB (Typ) [R-0.85/in]	0.098	0.900
Roxul Comfortbatt 3.5in [R-4.29/in]	0.019	0.900
Wood, Coniferous (Softwood) [R-1.03/in]	0.081	0.900