
R2 - Flat Roof

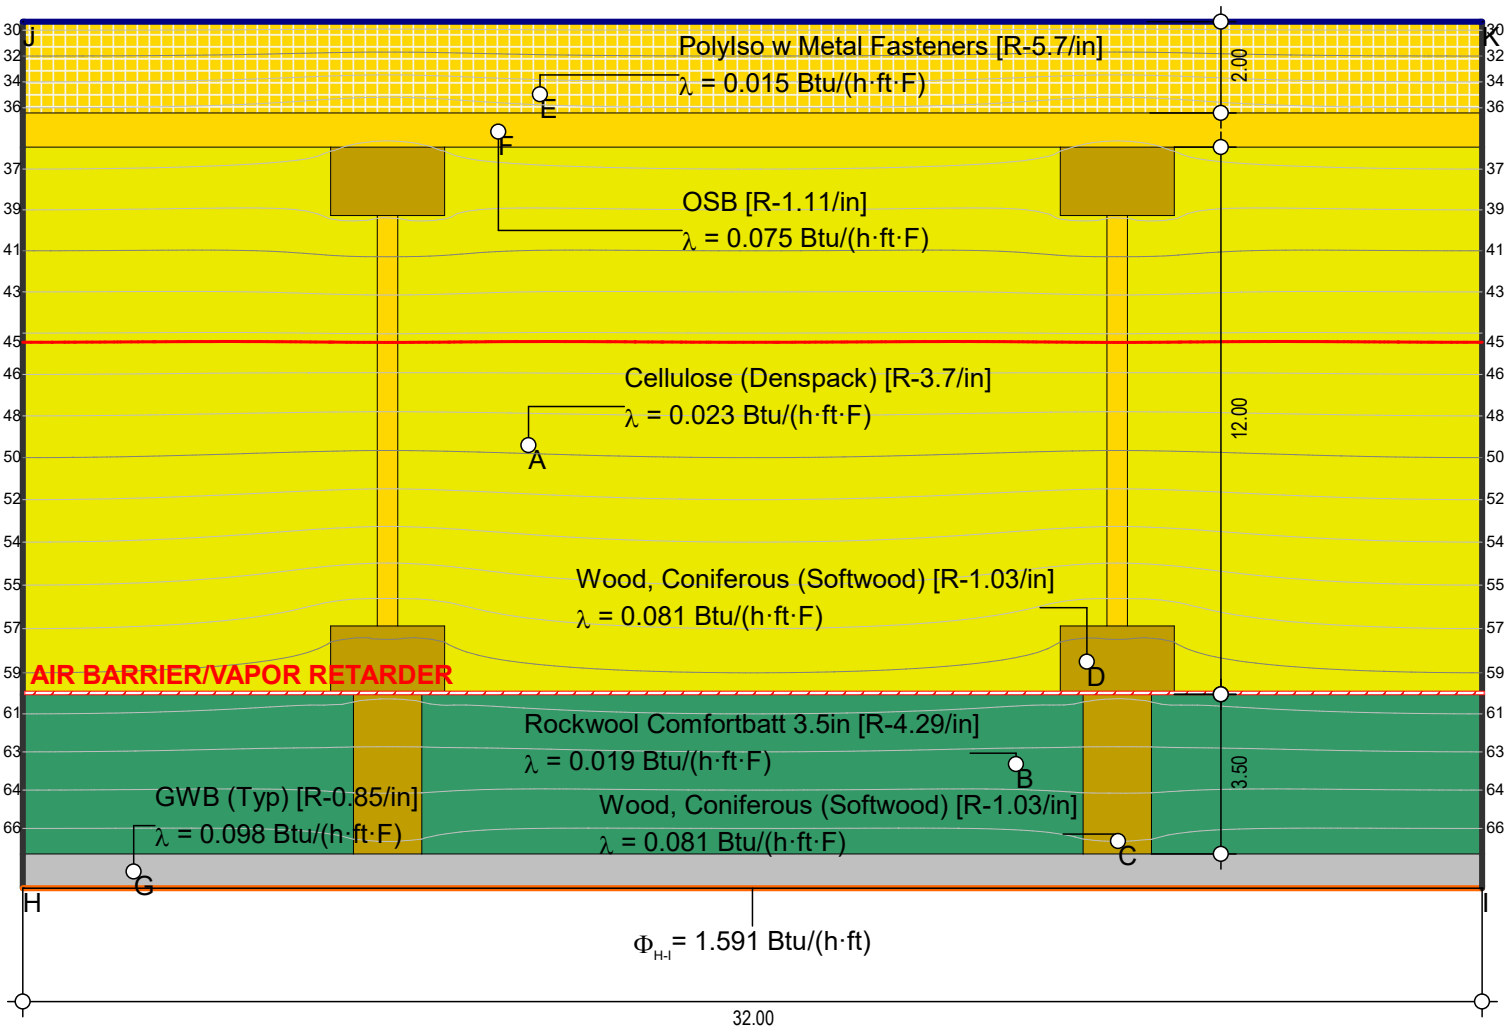

$$R_{eq\ H\text{-}I} = \frac{38.52 \cdot 2.667}{1.591} = 64.6\ F \cdot ft^2 \cdot h/Btu$$

Boundary Condition	q[Btu/(h·ft²)]	θ
Exterior, normal [Dutchess Co AP 90-day, -1.4C, 0.04 Rse]	29	
Interior, heat flux, upwards	68	
Symmetry/Model section	0.000	

Material	λ[Btu/(h·ft·F)]	ε
Cellulose (Denspack) [R-3.7/in]	0.023	0.900
GWB (Typ) [R-0.85/in]	0.098	0.900
OSB [R-1.11/in]	0.075	0.900
Polyiso w Metal Fasteners [R-5.7/in]	0.015	0.900
Rockwool Comfortbatt 3.5in [R-4.29/in]	0.019	0.900
Wood, Coniferous (Softwood) [R-1.03/in]	0.081	0.900