
S1 - Floor Slab

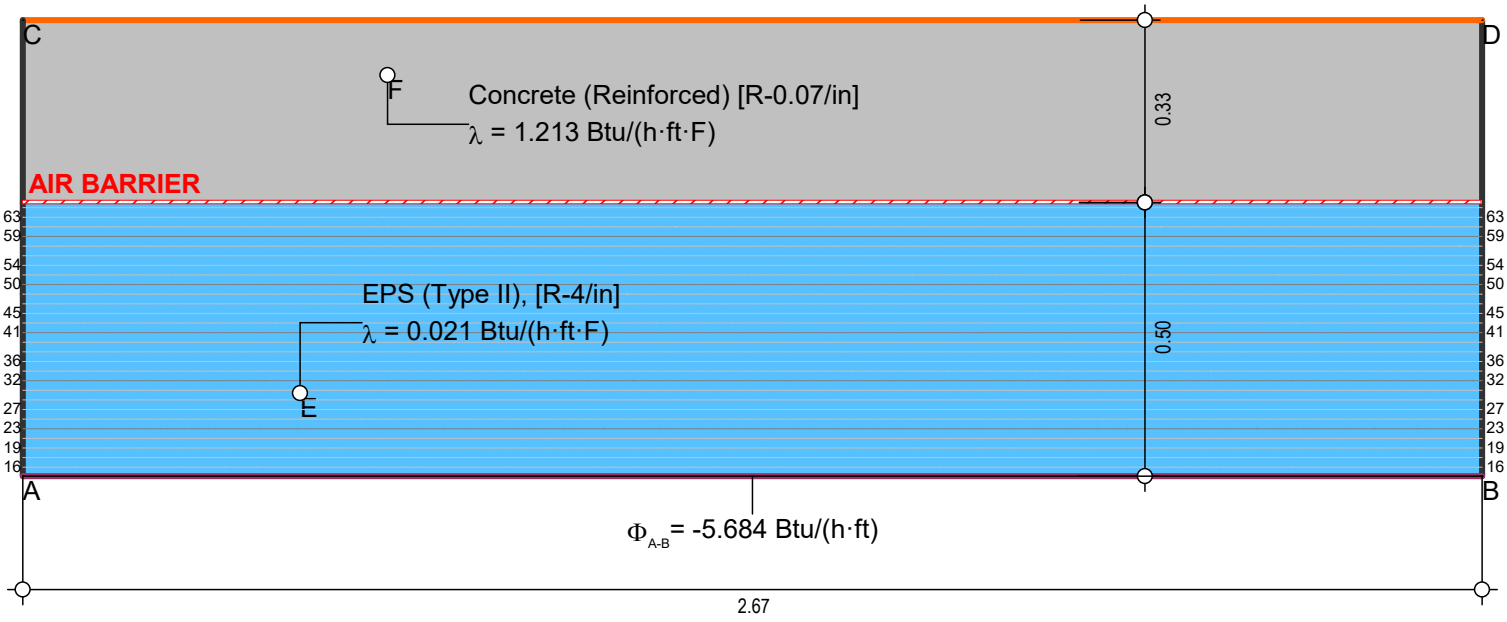

$$R_{eq\ A\text{-}B} = \frac{54.0 \cdot 2.667}{5.684} = 25.3\ F \cdot ft^2 \cdot h/Btu$$

Boundary Condition	θ[°F]	h[Btu/(h·ft²·F)]
Ext. No Rse	14.000	17.611
Interior, heat flux, downwards	68.000	1.036
Symmetry/Model section		

Material	λ[Btu/(h·ft·F)]	ε
Concrete (Reinforced) [R-0.07/in]	1.213	0.900
EPS (Type II), [R-4/in]	0.021	0.900