
W1 - Wood-framed Wall

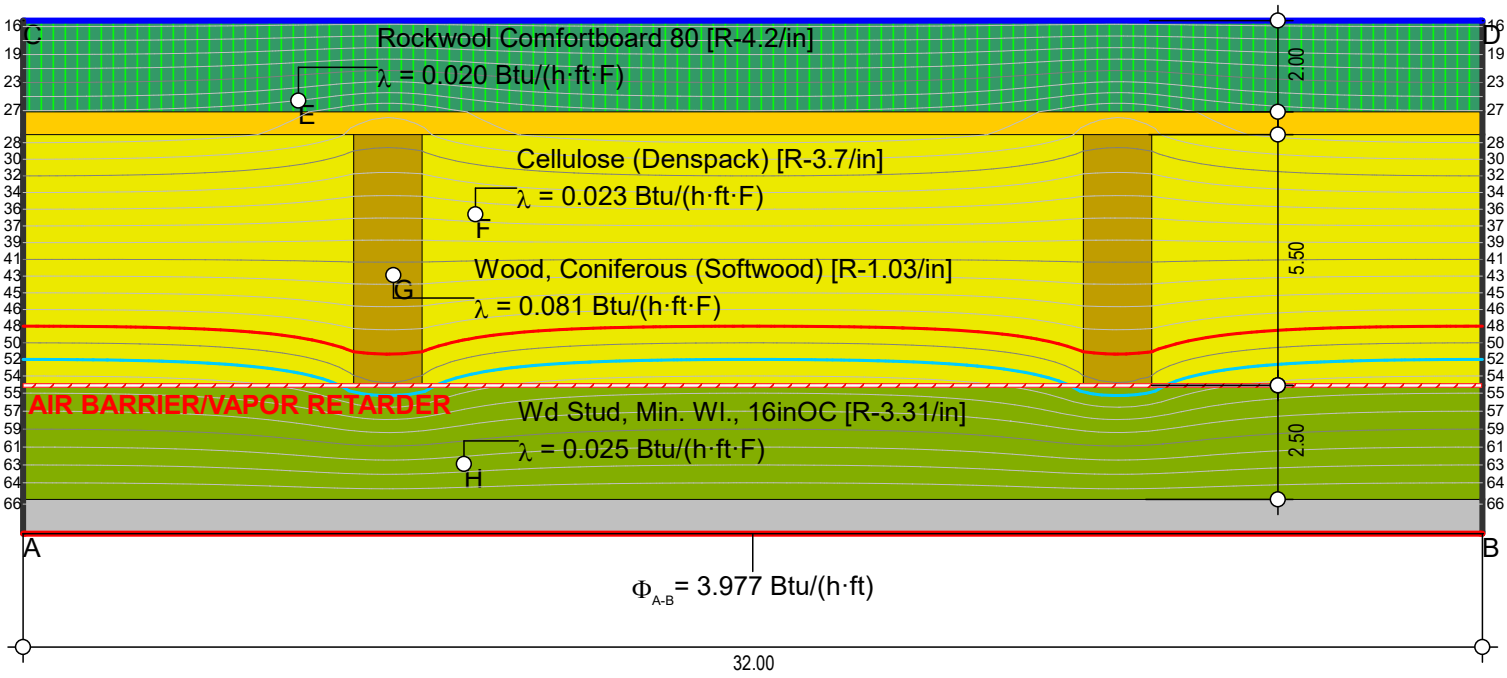

$$R_{eq\ A\text{-}B} = \frac{54.0 \cdot 2.667}{3.977} = 36.2\ F \cdot ft^2 \cdot h/Btu$$

Boundary Condition	q[Btu/(h·ft²)]	θ[°F]	h[Btu/(h·ft²·F
Exterior, ventilated		14.000	1.3
Interior, normal, horizontal		68.000	1.3
Symmetry/Model section	0.000		

Material	λ[Btu/(h·ft·F)]	ε
Cellulose (Denspack) [R-3.7/in]	0.023	0.900
GWB (Typ) [R-0.85/in]	0.098	0.900
OSB [R-1.11/in]	0.075	0.900
Rockwool Comfortboard 80 [R-4.2/in]	0.020	0.900
Wd Stud, Min. Wl., 16inOC [R-3.31/in]	0.025	0.900
Wood, Coniferous (Softwood) [R-1.03/in]	0.081	0.900