
R1 - Sloped Roof

VENTED ROOF ASSEMBLY

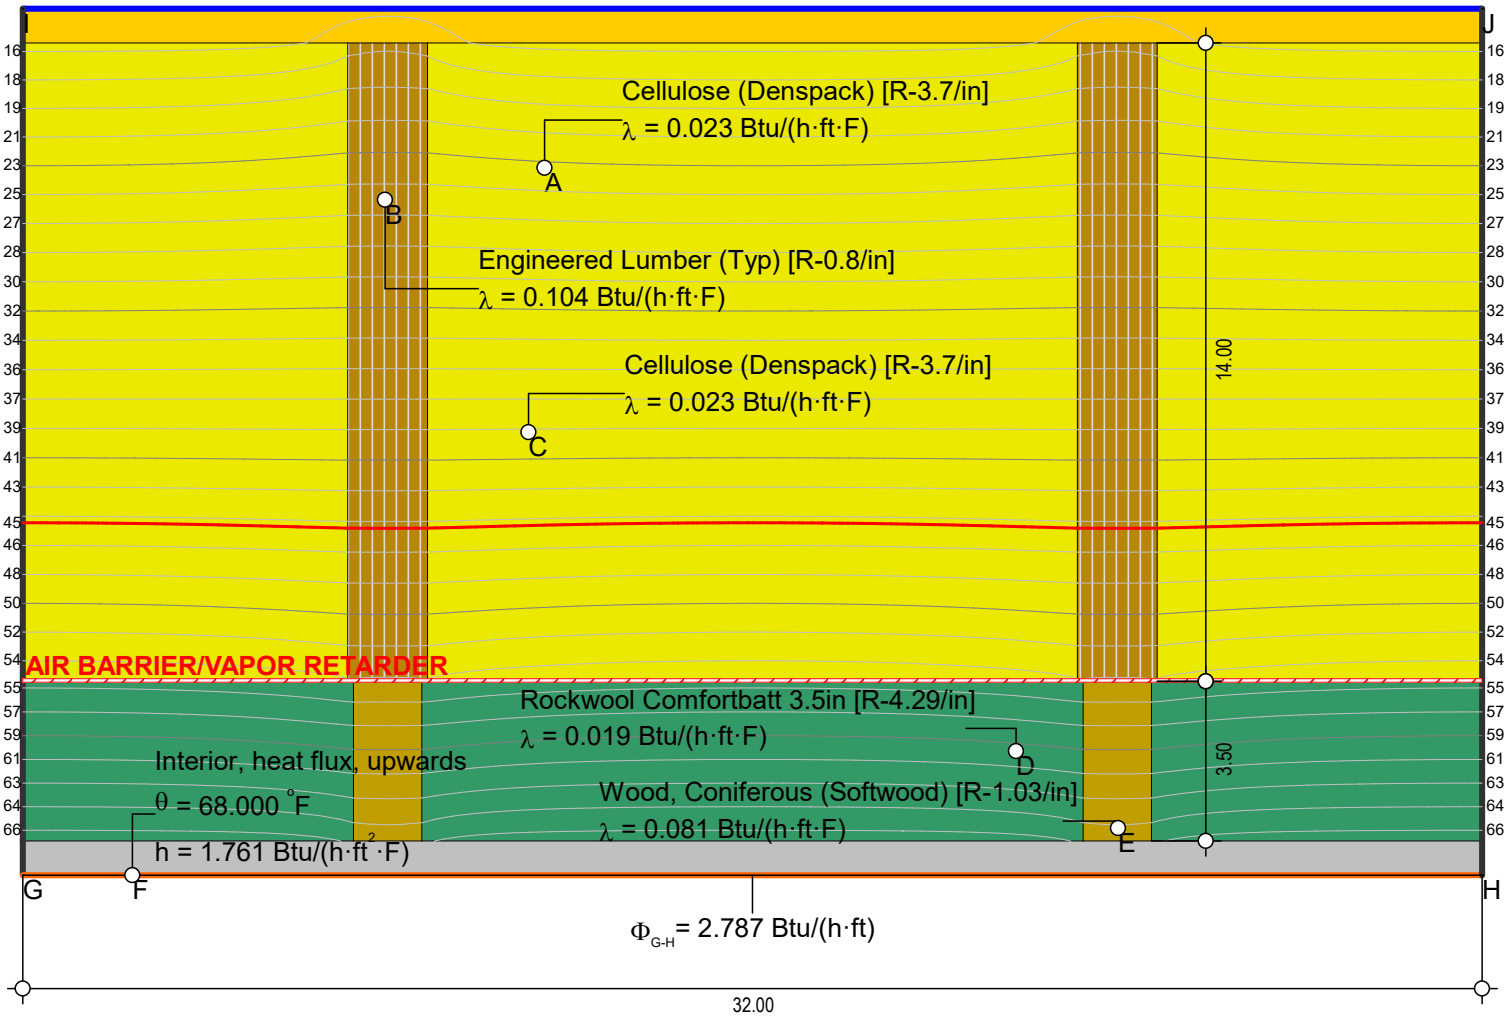

$$R_{eq\ G\text{-}H} = \frac{54.0 \cdot 2.667}{2.787} = 51.7\ F \cdot ft^2 \cdot h/Btu$$

Boundary Condition	q[Btu/(h·ft²)]	θ[°F]	h[Btu/(h·ft²·F)]
Exterior, ventilated		14.000	1.355
Interior, heat flux, upwards		68.000	1.761
Symmetry/Model section	0.000		

Material	λ[Btu/(h·ft·F)]	ε
Cellulose (Denspack) [R-3.7/in]	0.023	0.900
Engineered Lumber (Typ) [R-0.8/in]	0.104	0.900
GWB (Typ) [R-0.85/in]	0.098	0.900
OSB [R-1.11/in]	0.075	0.900
Rockwool Comfortbatt 3.5in [R-4.29/in]	0.019	0.900
Wood, Coniferous (Softwood) [R-1.03/in]	0.081	0.900